
AMPLIACIÓN CABAÑA – LAGO TODOS LOS SANTOS

Lámina 1: PLANTA · Bodega 3,50 × 2,50 m + terraza techada 4,75 m · Techo rectangular, esquinas a 90° · Medidas en metros · Borrador para revisión

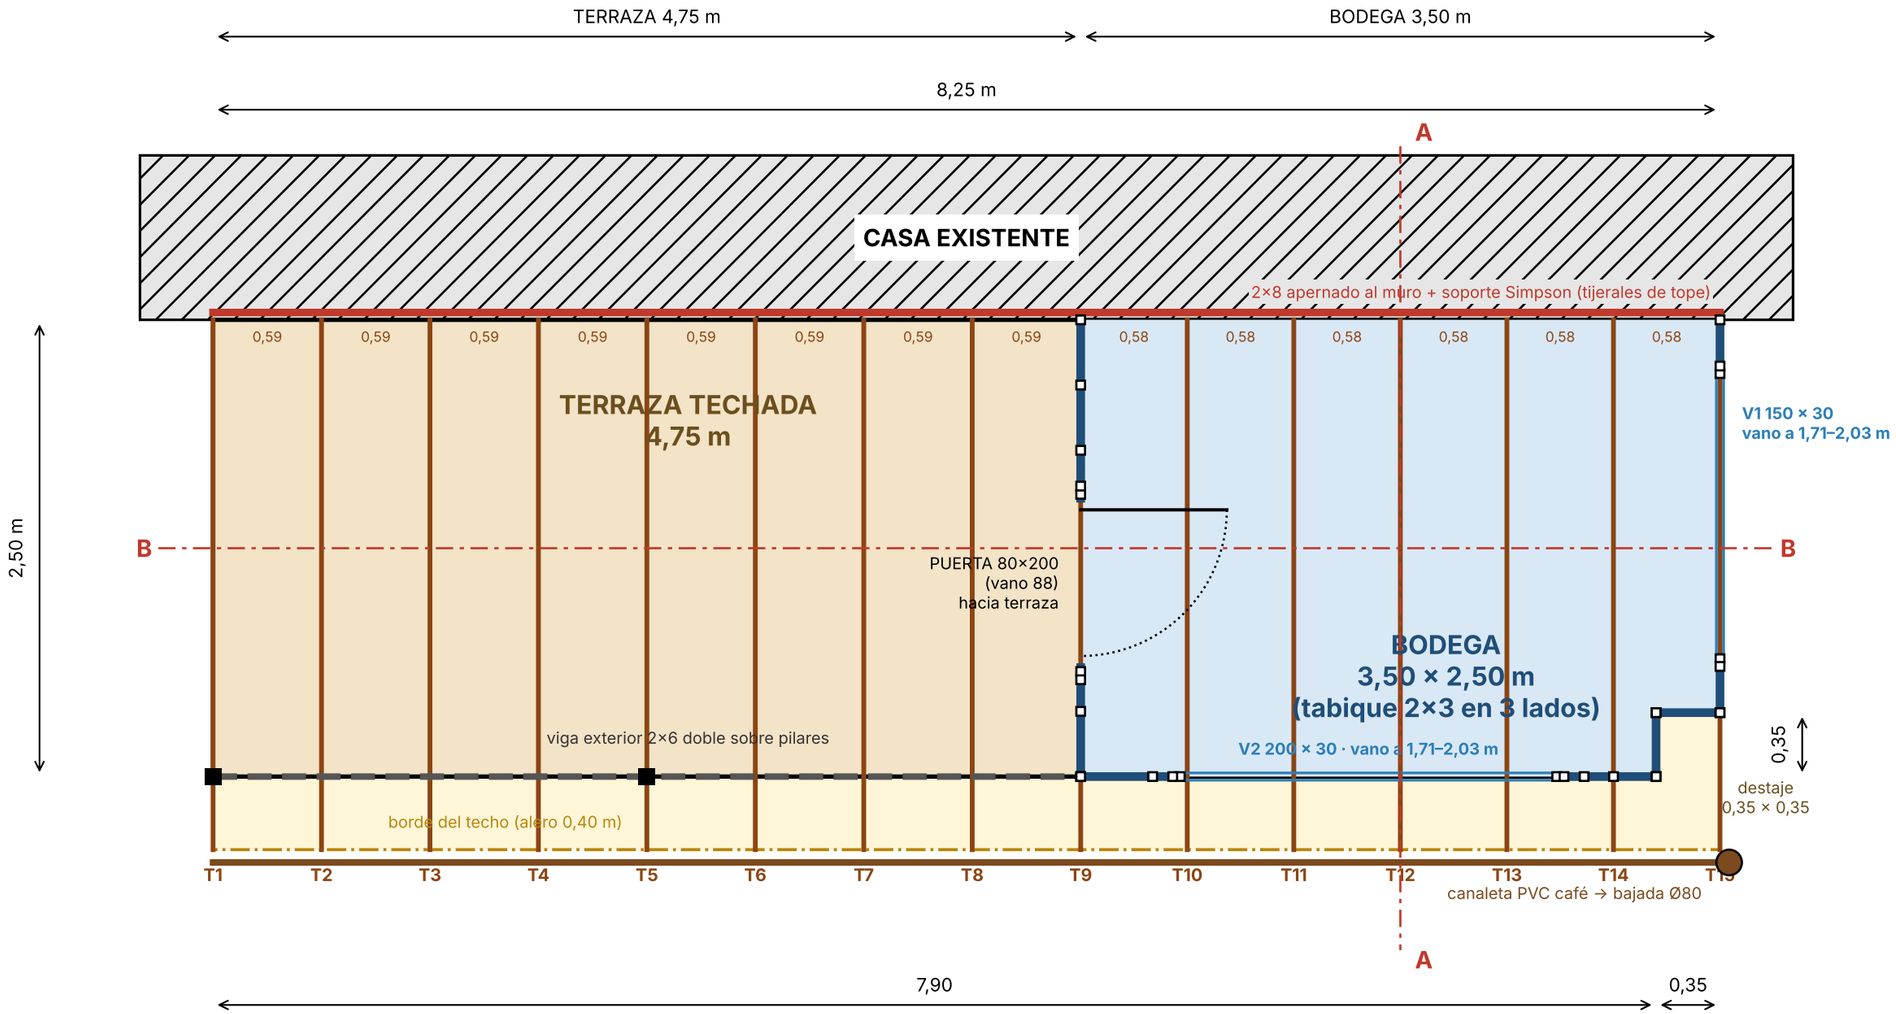

- Tijeral 2×6 pino IPV
- Tabique bodega 2×3 pino IPV (pies derechos c/40 cm)
- Viga exterior 2×6 doble (terraza)
- Borde de techo / tapacán
- 2×8 apernado al muro de la casa
- Canaleta aguas lluvia PVC café
- ☐ Pie derecho
- ■ Pilar terraza 4×4

Tijerales (largo inclinado, incluye alero)


Tijeral	Posición (m)	Largo (m)	Nota
T1	0.00	2.87	entero
T2	0.59	2.87	entero
T3	1.19	2.87	entero
T4	1.78	2.87	entero
T5	2.38	2.87	entero
T6	2.97	2.87	entero
T7	3.56	2.87	entero
T8	4.16	2.87	entero
T9	4.75	2.87	entero
T10	5.33	2.87	entero
T11	5.92	2.87	entero
T12	6.50	2.87	entero
T13	7.08	2.87	entero
T14	7.67	2.87	entero
T15	8.25	2.87	entero

Cubierta trapezoidal (ancho útil ~1,0 m) · lista completa en lámina 4

Plancha	Desde – hasta (m)	Tipo	Largo (m)
P1	0.0 – 1.00	Translúcida	3.00
P2	1.0 – 2.00	Translúcida	3.00
P3	2.0 – 3.00	Translúcida	3.00
P4	3.0 – 4.00	Translúcida	3.00
P5	4.0 – 5.00	Translúcida	3.00
P6	5.0 – 6.00	OPACA	3.00
P7	6.0 – 7.00	Translúcida	3.00
P8	7.0 – 8.00	OPACA	3.00
P9	8.0 – 8.25	Translúcida	3.00

AMPLIACIÓN CABAÑA – LAGO TODOS LOS SANTOS

Lámina 2: ISOMÉTRICO (vista desde afuera, casa existente atrás en gris) · Bodega 3,50 × 2,50 m + terraza techada 4,75 m · Techo rectangular, esquinas a 90° · Medidas en metros · Borrador para revisión

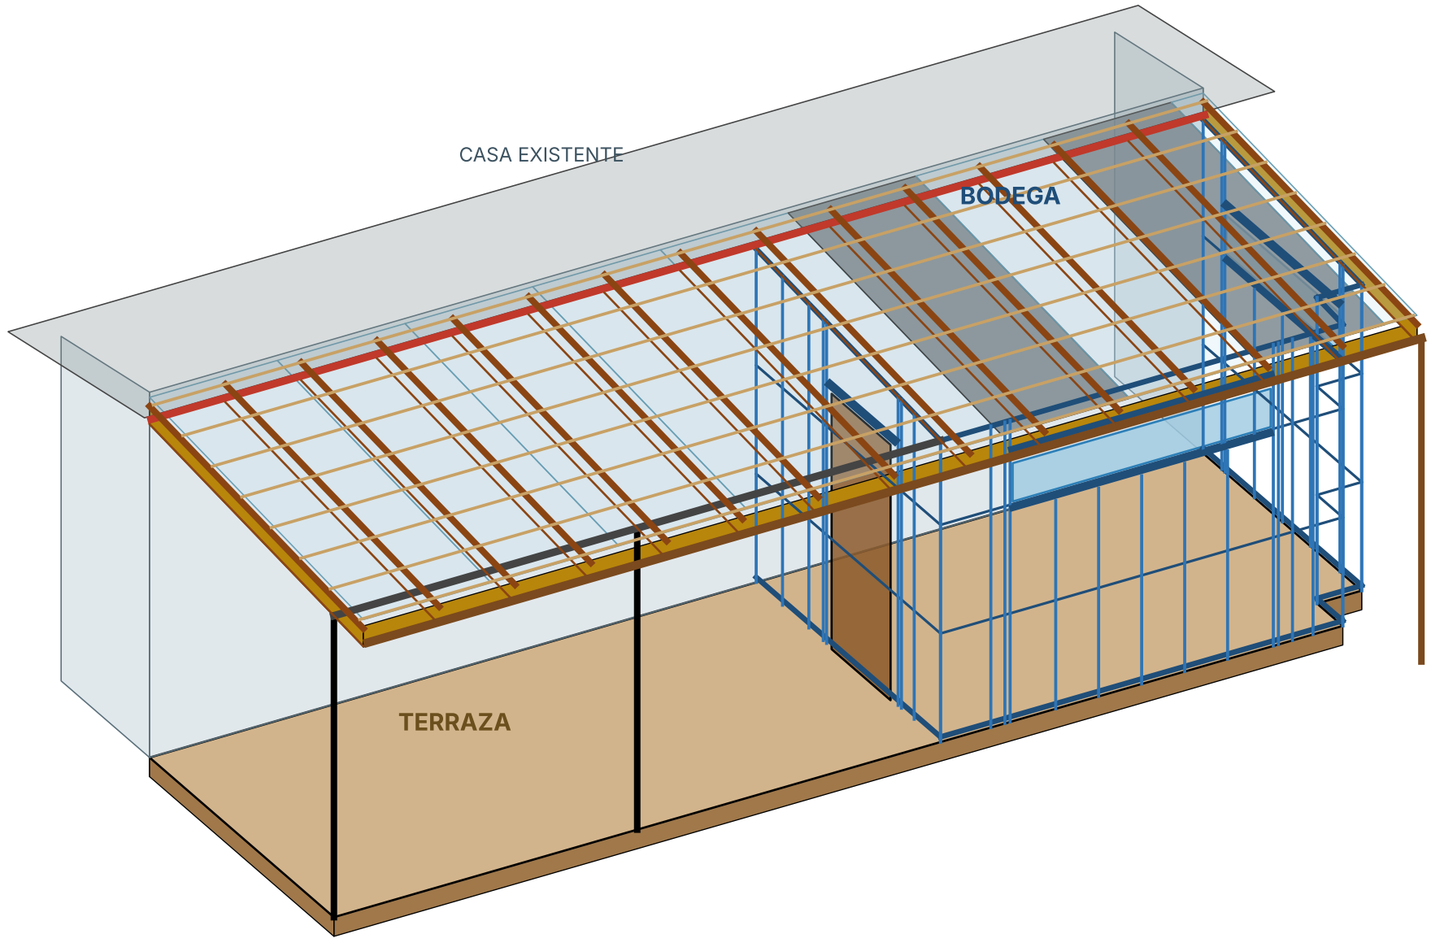


Tijerales 2×6 c/60 cm · alero 40 cm · cubierta trapezoidal translúcida en terraza e intercalada en bodega · pendiente ≈ 10 % · viga 2×8 apernada al muro (rojo) · canaleta PVC café

AMPLIACIÓN CABAÑA – LAGO TODOS LOS SANTOS

Lámina 3: CORTES · Bodega 3,50 × 2,50 m + terraza techada 4,75 m · Techo rectangular, esquinas a 90° · Medidas en metros · Borrador para revisión


CORTE TRANSVERSAL A-A (por la bodega)

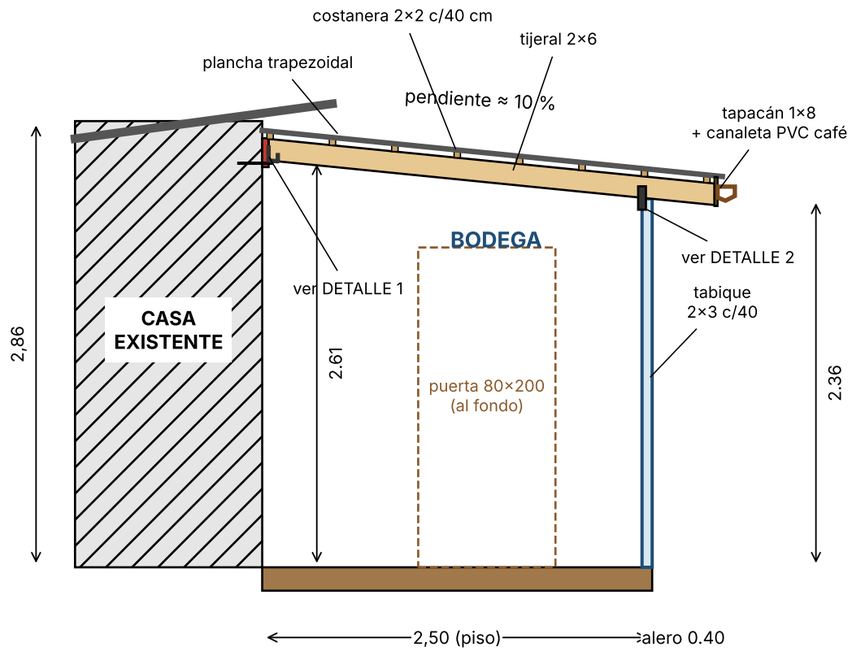


NOTAS

1. Alturas en metros desde el piso de la ampliación.
2. Junto a la casa: tijeral 2×6 DE TOPE contra viga 2×8 (41×185) apernada al muro, enrasada arriba con el tijeral, con soporte viga Simpson 2×6 ZMAX. Por fuera: sobre muro de bodega o viga 2×6 doble, con 2 soportes sismo y viento Simpson H3 por tijeral (uno por lado).
3. ALTURA MURO EXTERIOR: 2,36 m bajo el tijeral (CONFIRMADA). Así el techo pasa bajo el alero existente (2,86 m) con ≈10 % de pendiente.
4. Costaneras 2×2 c/40 cm; plancha en una sola pieza, vuela 8 cm sobre la canaleta (DET. 5).
5. Tijerales 2×6 pino IPV cada 60 cm. Cubierta translúcida en terraza e intercalada (translúcida / opaca) en bodega.
6. Bodega: tabique 2×3 IPV c/40 cm en 3 lados (contra la casa no lleva tabique), 2 corridas de cadenetas y puerta 80×200 hacia la terraza.


DETALLE 1 · apoyo en muro de la casa

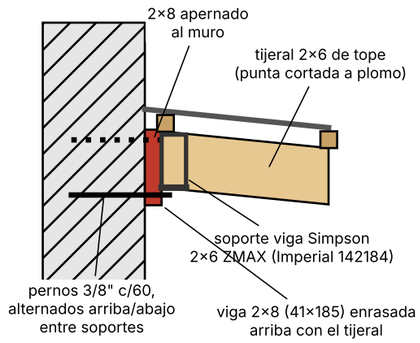

DETALLE 2 · apoyo en muro exterior

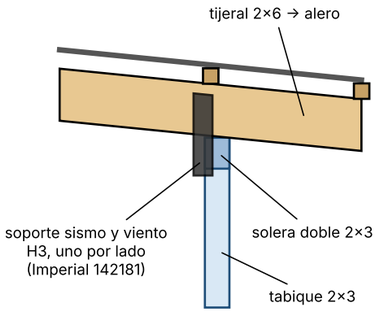

CORTE LONGITUDINAL B-B (a 1.25 m del muro, mirando hacia la casa)

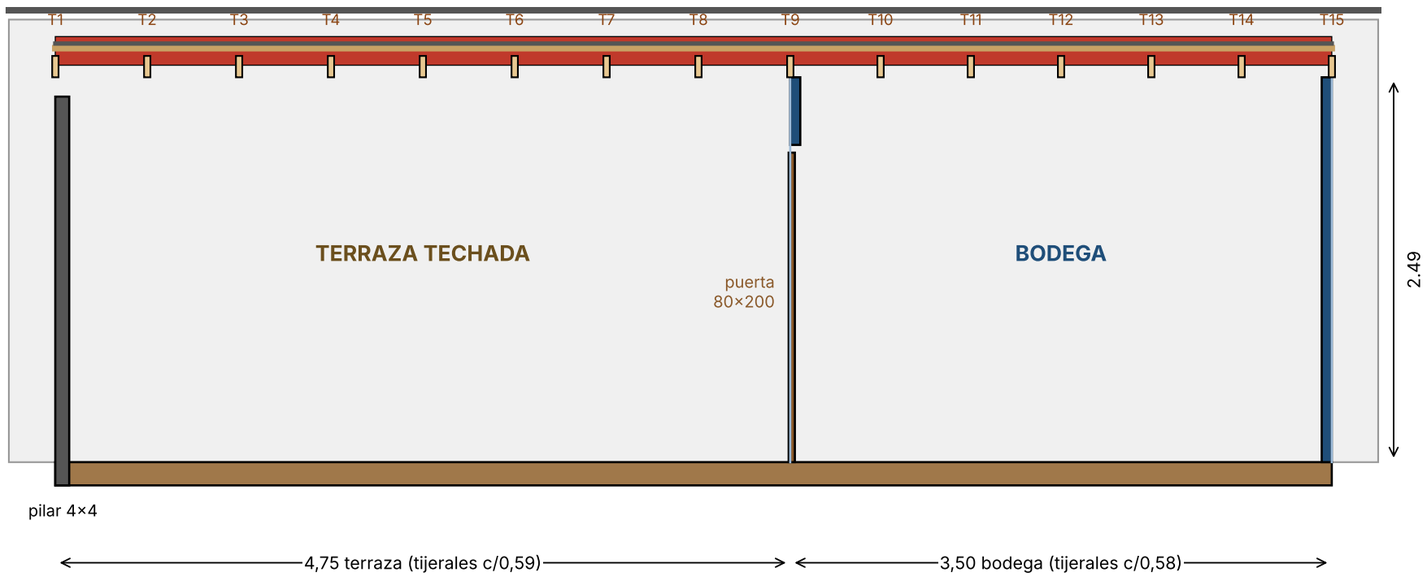

AMPLIACIÓN CABAÑA – LAGO TODOS LOS SANTOS

Lámina 4: LISTA DE MATERIALES · Bodega 3,50 × 2,50 m + terraza techada 4,75 m · Techo rectangular, esquinas a 90° · Medidas en metros · Borrador para revisión

Ítem	Material / medida	Cant.	Nota
ESTRUCTURA DE TECHO			
Tijerales c/60 cm	Pino IPV 2×6 × 3,20	15	todos iguales, 2,87 m
Viga 2×8 apernada al muro (tijerales de tope)	Pino IPV 2×8 × 3,20	3	de canto, enrasada con tijeral
Pernos o tirafondos 3/8"	c/60 cm	15	según material del muro existente
Soporte viga madera cepillada 2×6 ZMAX	Simpson · Imperial SKU 142184	15	1 por tijeral, en muro casa
Soporte sismo y viento H3	Simpson · Imperial SKU 142181	30	2 por tijeral (uno por lado)
Costaneras c/40 cm	Pino IPV 2×2 × 3,20	23	8 corridas
Tapacán vertical	Tabla pino 1×8 × 3,20	3	8,25 m recto; pintar
Bloqueos entre tijerales (muro bodega)	Pino IPV 2×6 × 3,20	1	
TERRAZA			
Viga exterior doble (recta, 4,75 m)	Pino IPV 2×6 × 3,20	4	unir sobre pilar
Pilares	Pino IPV 4×4 × 3,20	2	
PISO TERRAZA (completar rectángulo)			
Ampliación de piso (triángulo de la diagonal)	según piso existente	~2,4 m²	POR DEFINIR: falta estructura del piso
CUBIERTA TRAPEZOIDAL			
Plancha translúcida (policarbonato)	largos: 3.00, 3.00, 3.00, 3.00, 3.00, 3.0	7	mismo perfil que la opaca
Plancha opaca (zinc-alum)	largos: 3.00, 3.00	2	intercalada en bodega
HOJALATERÍA DE REMATE (zincalum 0,4 mm)			
Plancha lisa para plegar	zincalum 1,00 × 3,00 m	3	el hojalatero pliega forros y remates
Forro contra muro existente	desarrollo ~40 cm x 3 m	3	8,25 m + traslapos (DETALLE 3)
Remate lateral	desarrollo ~35 cm	2	2 × 2,9 m (DETALLE 4)
Cierre de espuma perfil trapezoidal	tira ~1 m	9	bajo el forro, junto al muro
Sellante poliuretano	cartucho	2	borde superior del forro
AGUAS LLUVIA (PVC café)			
Canaleta PVC café 110 mm	x 4,00 m	3	8,25 m de borde recto
Uniones de canaleta	PVC café	2	
Tapas de canaleta	PVC café	2	
Salida a bajada	PVC café Ø80	1	extremo derecho (esquina bodega)
Ganchos de canaleta	PVC café	19	c/50 cm, al tapacán 1×8
Tubo de bajada	PVC café Ø80 × 3 m	2	confirmar altura al terreno
Codos de bajada	PVC café Ø80	3	2 para el alero + 1 al final
Abrazaderas de bajada	PVC café Ø80	3	
Sellante para PVC / silicona	cartucho	1	


Ítem	Material / medida	Cant.	Nota
BODEGA – ESTRUCTURA			
Pies derechos c/40 cm	Pino IPV 2×3 × 3,20	31	incluye vano y esquinas
Soleras (inferior + superior doble)	Pino IPV 2×3 × 3,20	9	
Cadenetas (2 corridas)	Pino IPV 2×3 × 3,20	6	
Dintel puerta (de canto)	Pino IPV 2×4 × 3,20	1	
Puerta exterior + marco	80 × 200 cm	1	bisagras 3 × 3½" + cerradura
Escuadras metálicas base pilares	galvanizadas	4	2 por pilar
TORNILLOS (sin clavos · detalle en planilla Excel)			
Tornillo madera 8 × 3" zincado		990	
Tirafondo 1/4" x 4" zincado		40	
Tornillo Simpson SD #9 × 1½" (para conectores)		430	
Tirafondo 3/8" x 4½" + golilla		20	
Autoperforante techo punta aguja 12 × 1½" c/golilla		370	
Autoperforante costura 1/4" x 7/8"		70	
Tornillo exterior 8 × 2" galvanizado		700	
Tornillo madera 6 × 1¼"		330	
Tornillo 6 × 1" (cortagotera)		20	
VENTANAS (2)			
Ventana V1 (muro lateral 2,5 m)	aluminio 150 × 30 cm	1	vano 152 × 32; borde sup. ~2,0 m
Ventana V2 (muro frente a la casa)	aluminio 200 × 30 cm	1	vano 202 × 32; borde sup. ~2,0 m
Dintel V2 (de canto)	Pino IPV 2×8 × 3,20	1	2,10 m, recibe 3 tijerales
Dintel V1 (de canto)	Pino IPV 2×6 × 3,20	1	1,60 m
Refuerzos: antepecho doble, muñecos, calce	Pino IPV 2×3 × 3,20	12	jambas y p.d. enteros ya incluidos arriba
Botaguas sobre ventanas	zincalum (de las planchas lisas)	2	con sello
Silicona neutra exterior	cartucho	1	sello perimetral ventanas
BODEGA – REVESTIMIENTOS			
SmartPanel exterior	1,22 × 2,44	11	~18 m², pintar
Contrachapado ranurado interior	1,22 × 2,44	10	~18 m² (sin muro de la casa)
Barrera de humedad (Tyvek/fieltro)	rollo	1	detrás del SmartPanel
Esquineros / tapajuntas	2,40 m	6	incluye las 2 esquinas del destaje
Cortagotera en Z	3,00 m	3	unión de franja superior
Grapas para barrera de humedad	caja	1	corchetera

Cantidades de madera con ~10 % de pérdida (tijerales justos). Confirmar ancho útil y largos disponibles de las planchas en la tienda.


AMPLIACIÓN CABAÑA – LAGO TODOS LOS SANTOS

Lámina 5: HOJALATERÍA DE REMATE · Bodega 3,50 × 2,50 m + terraza techada 4,75 m · Techo rectangular, esquinas a 90° · Medidas en metros · Borrador para revisión


UBICACIÓN DE LA HOJALATERÍA (planta de techo)

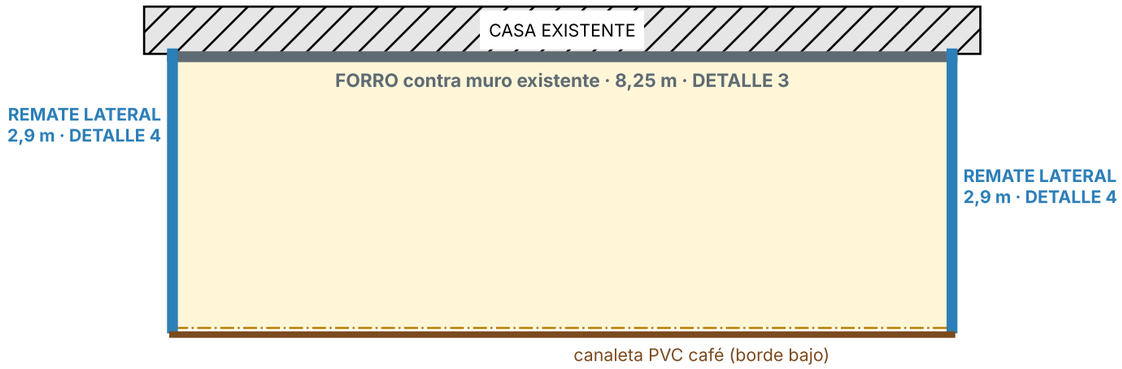

DETALLE 3 · forro contra el muro existente

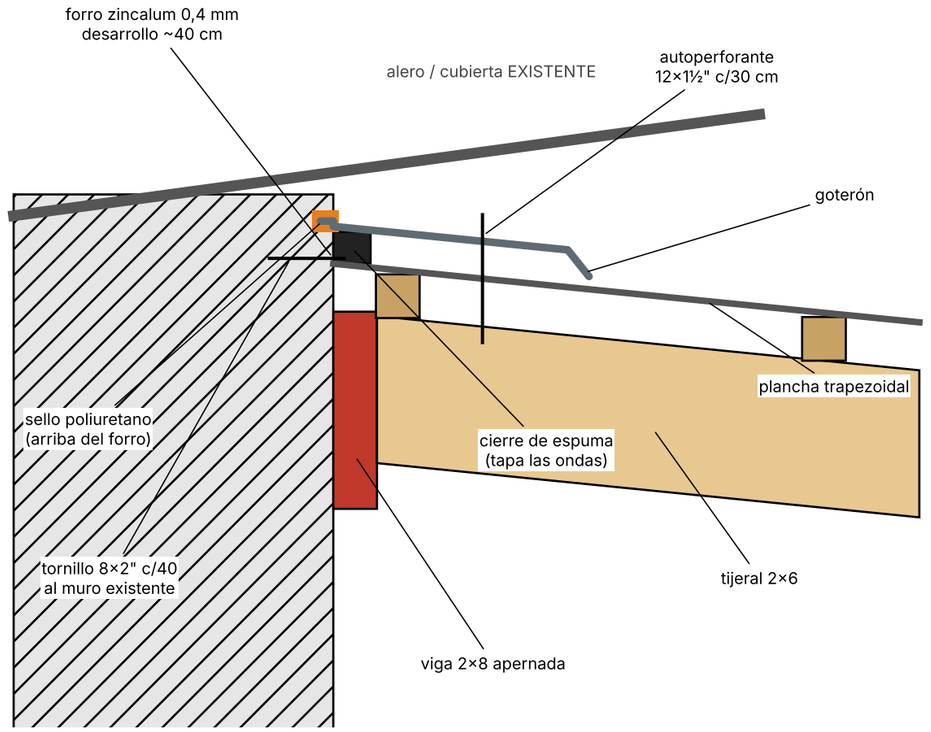

DETALLE 4 · remate lateral (los dos bordes de 2,5 m)

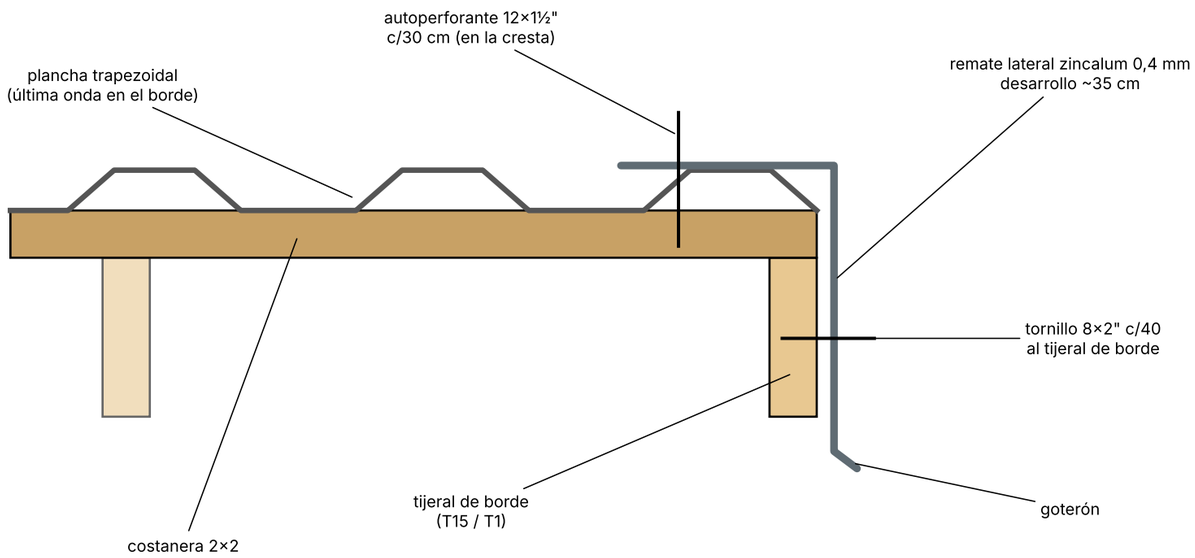


NOTAS HOJALATERÍA

1. Hojalatería en zincalum liso 0,4 mm, plegada por hojalatero.
2. FORRO (DETALLE 3): va contra el muro existente, bajo el alero de la casa, en los 8,25 m. Baja por el muro y monta ~20 cm sobre la plancha. Arriba lleva sello de poliuretano; abajo, goterón.
3. Bajo el forro, una tira de cierre de espuma tapa las ondas de la plancha trapezoidal para que no entre agua ni viento.
4. REMATE LATERAL (DETALLE 4): en los dos bordes perpendiculares a la casa (2,9 m cada uno). Cubre la última onda y baja por la cara del tijeral de borde, con goterón.
5. Traslapos entre piezas de hojalatería: mínimo 10 cm, con sello.
6. Fijación: autoperforante 12×1½" con golilla en la cresta (c/30 cm) y tornillo exterior 8×2" al muro / tijeral (c/40 cm). Sin clavos.


AMPLIACIÓN CABAÑA – LAGO TODOS LOS SANTOS

Lámina 6: VENTANAS, REFUERZOS Y CANALETA · Bodega 3,50 × 2,50 m + terraza techada 4,75 m · Techo rectangular, esquinas a 90° · Medidas en metros · Borrador para revisión

ELEVACIÓN MURO LATERAL (2,5 m) · ventana V1 150 × 30 — vista desde afuera

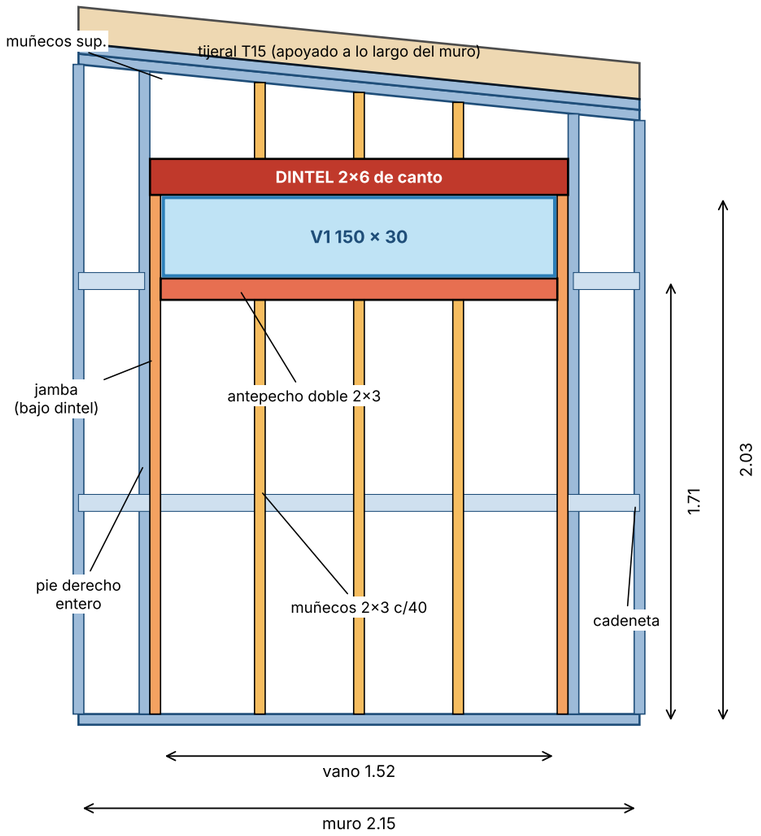


ELEVACIÓN MURO FRENTE A LA CASA · ventana V2 200 × 30 — vista desde afuera

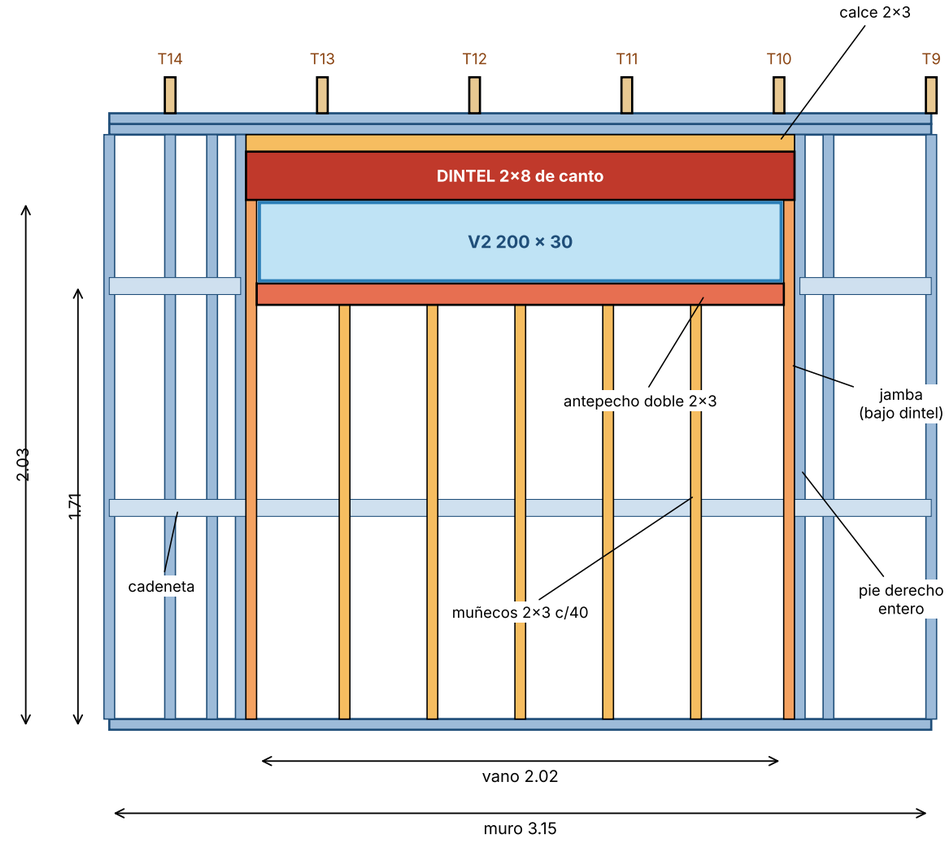

REFUERZOS EN CADA VANO DE VENTANA

1. A cada lado del vano: un PIE DERECHO ENTERO (de solera a solera) + una JAMBA pegada a él, que sostiene el dintel.
2. DINTEL de canto sobre las jambas: V2 (2,0 m) en 2×8 porque recibe los tijerales T10 a T13; V1 (1,5 m) en 2×6. Sobre el dintel: en V2 un calce 2×3 hasta la solera; en V1 muñecos cortos (el muro sube con la pendiente).
3. ANTEPECHO DOBLE 2×3 tendido bajo la ventana, a 1,71 m; bajo él, MUÑECOS 2×3 cada 40 cm (siguen la modulación).
4. Los pies derechos que caían dentro del vano se reemplazan por los muñecos. La corrida alta de cadenetas (1,70 m) se interrumpe en el vano: el antepecho hace ese trabajo.
5. Ventanas centradas en cada muro: V1 en el muro lateral de 2,50 m; V2 en el muro de 3,50 m.
6. Borde superior del vano a 2,03 m (ventana ~2,0 m, alineada con la puerta). No puede ir el antepecho a 2,0 m: no queda altura para el dintel bajo los tijerales (el muro exterior mide 2,36 m).
7. Ventanas de aluminio (fijas o proyectantes) a medida, con botaguas de zincalum arriba y sello de silicona.


DETALLE 5 · canaleta en el alero (borde bajo)

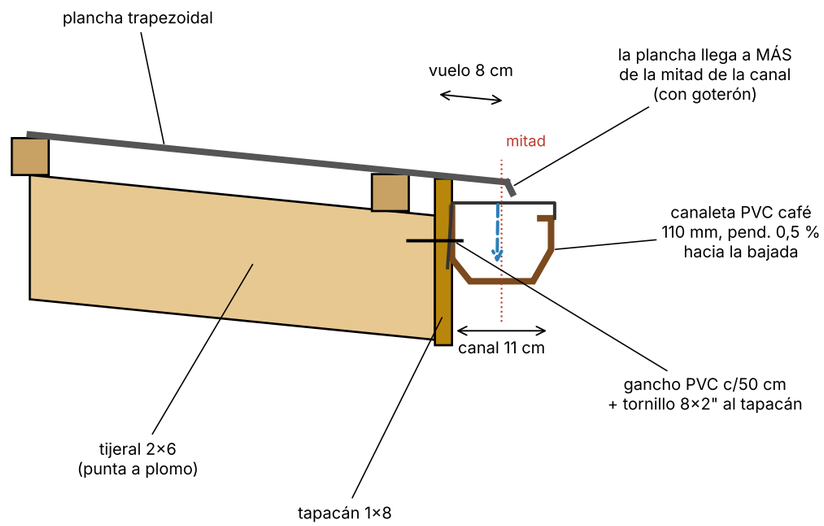

AMPLIACIÓN CABAÑA – LAGO TODOS LOS SANTOS

Lámina 7: FACHADA LATERAL BODEGA · Bodega 3,50 × 2,50 m + terraza techada 4,75 m · Techo rectangular, esquinas a 90° · Medidas en metros · Borrador para revisión


FACHADA LATERAL DE LA BODEGA (lado opuesto a la puerta) — vista desde afuera

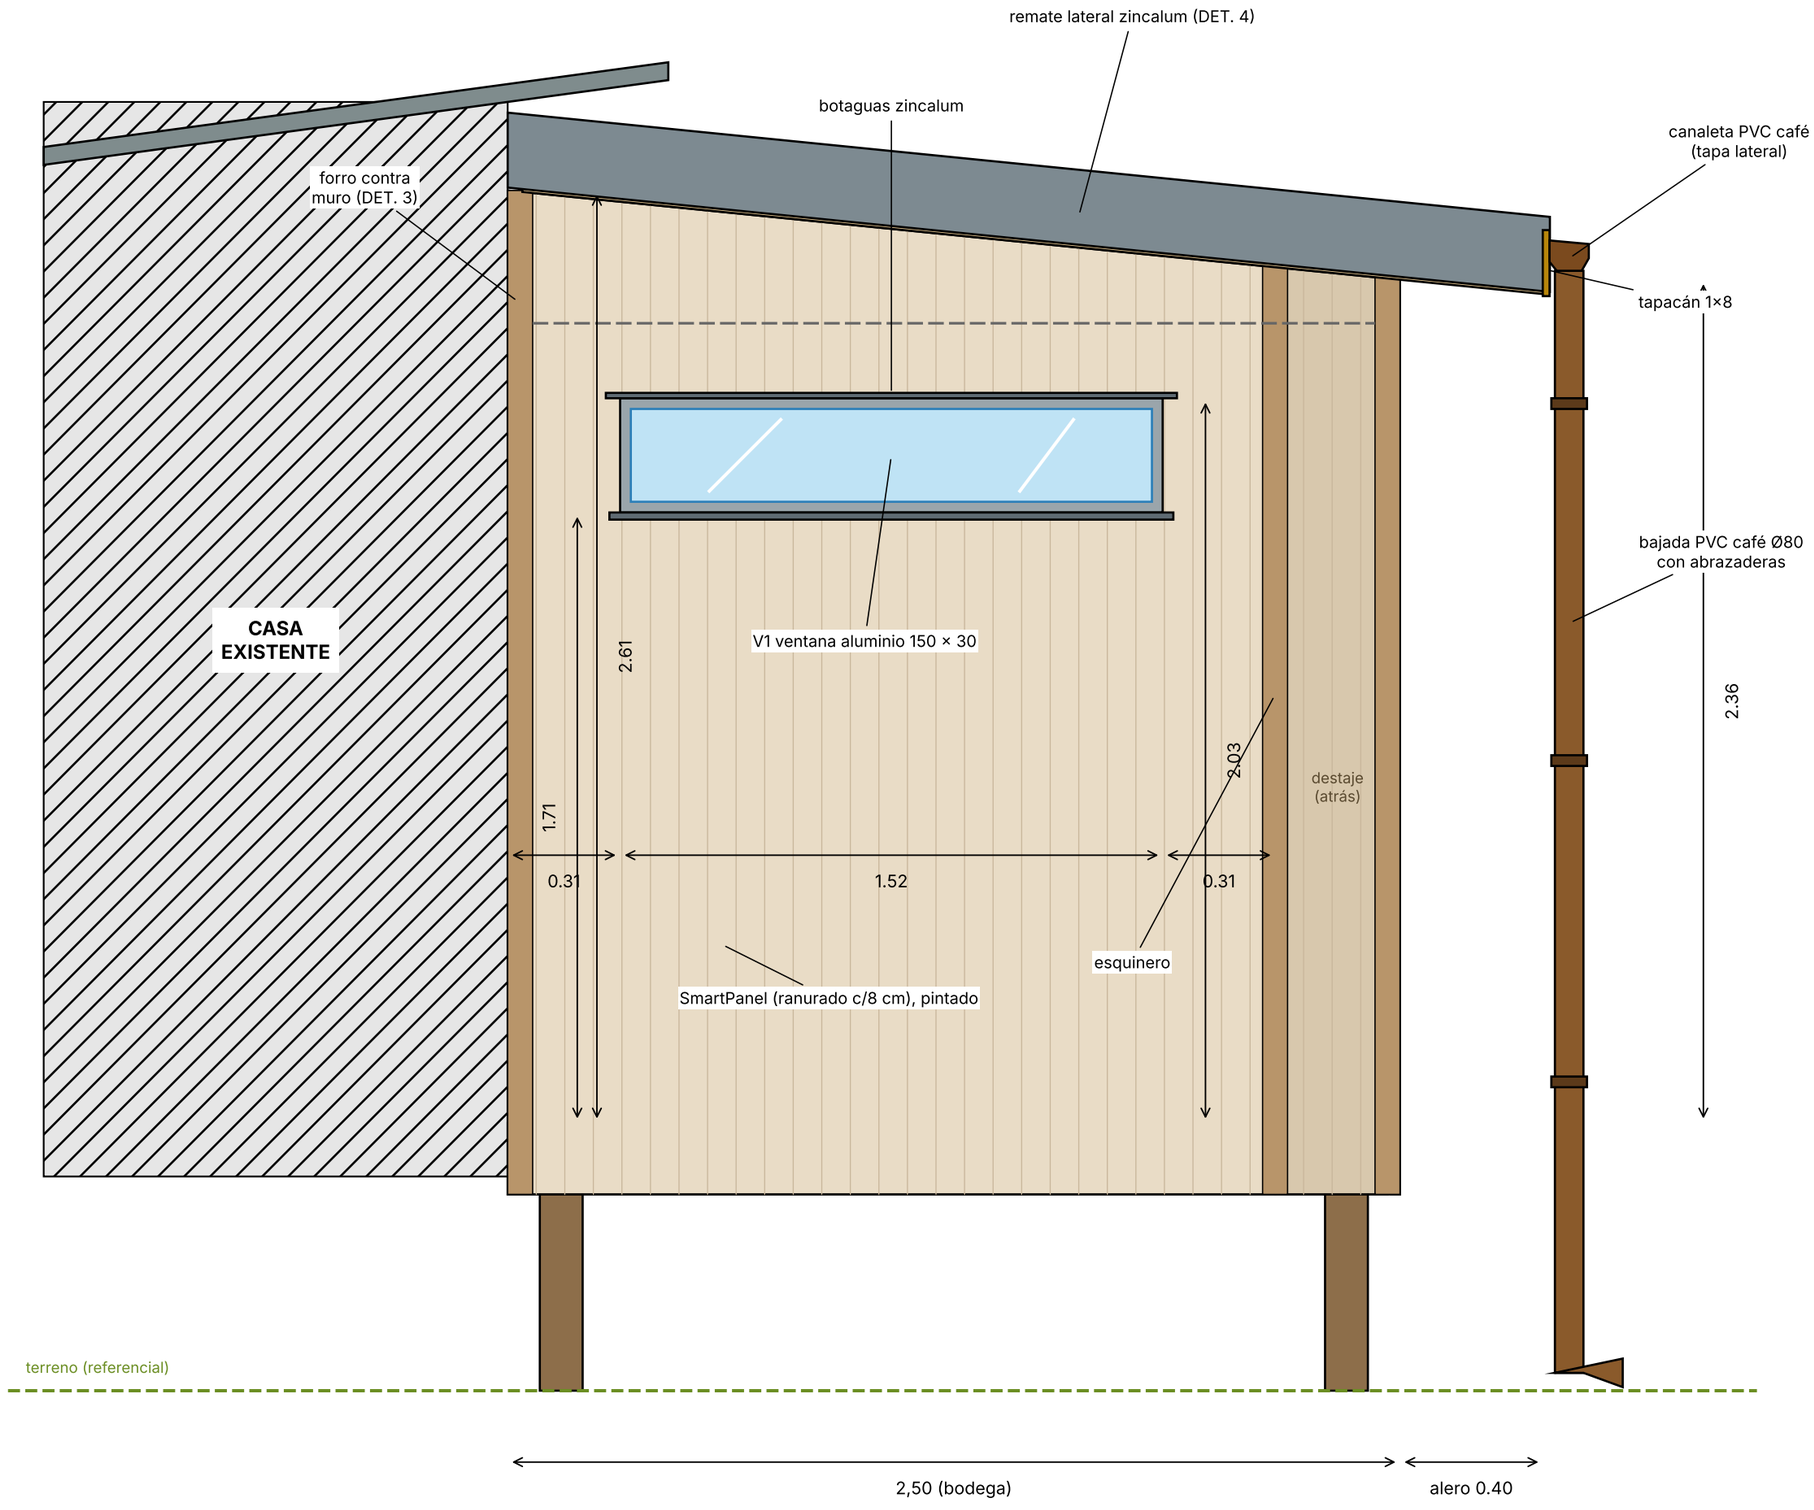

AMPLIACIÓN CABAÑA – LAGO TODOS LOS SANTOS

Lámina 8: FACHADA PRINCIPAL · Bodega 3,50 × 2,50 m + terraza techada 4,75 m · Techo rectangular, esquinas a 90° · Medidas en metros · Borrador para revisión


FACHADA PRINCIPAL (muro largo, frente opuesto a la casa) — vista desde afuera

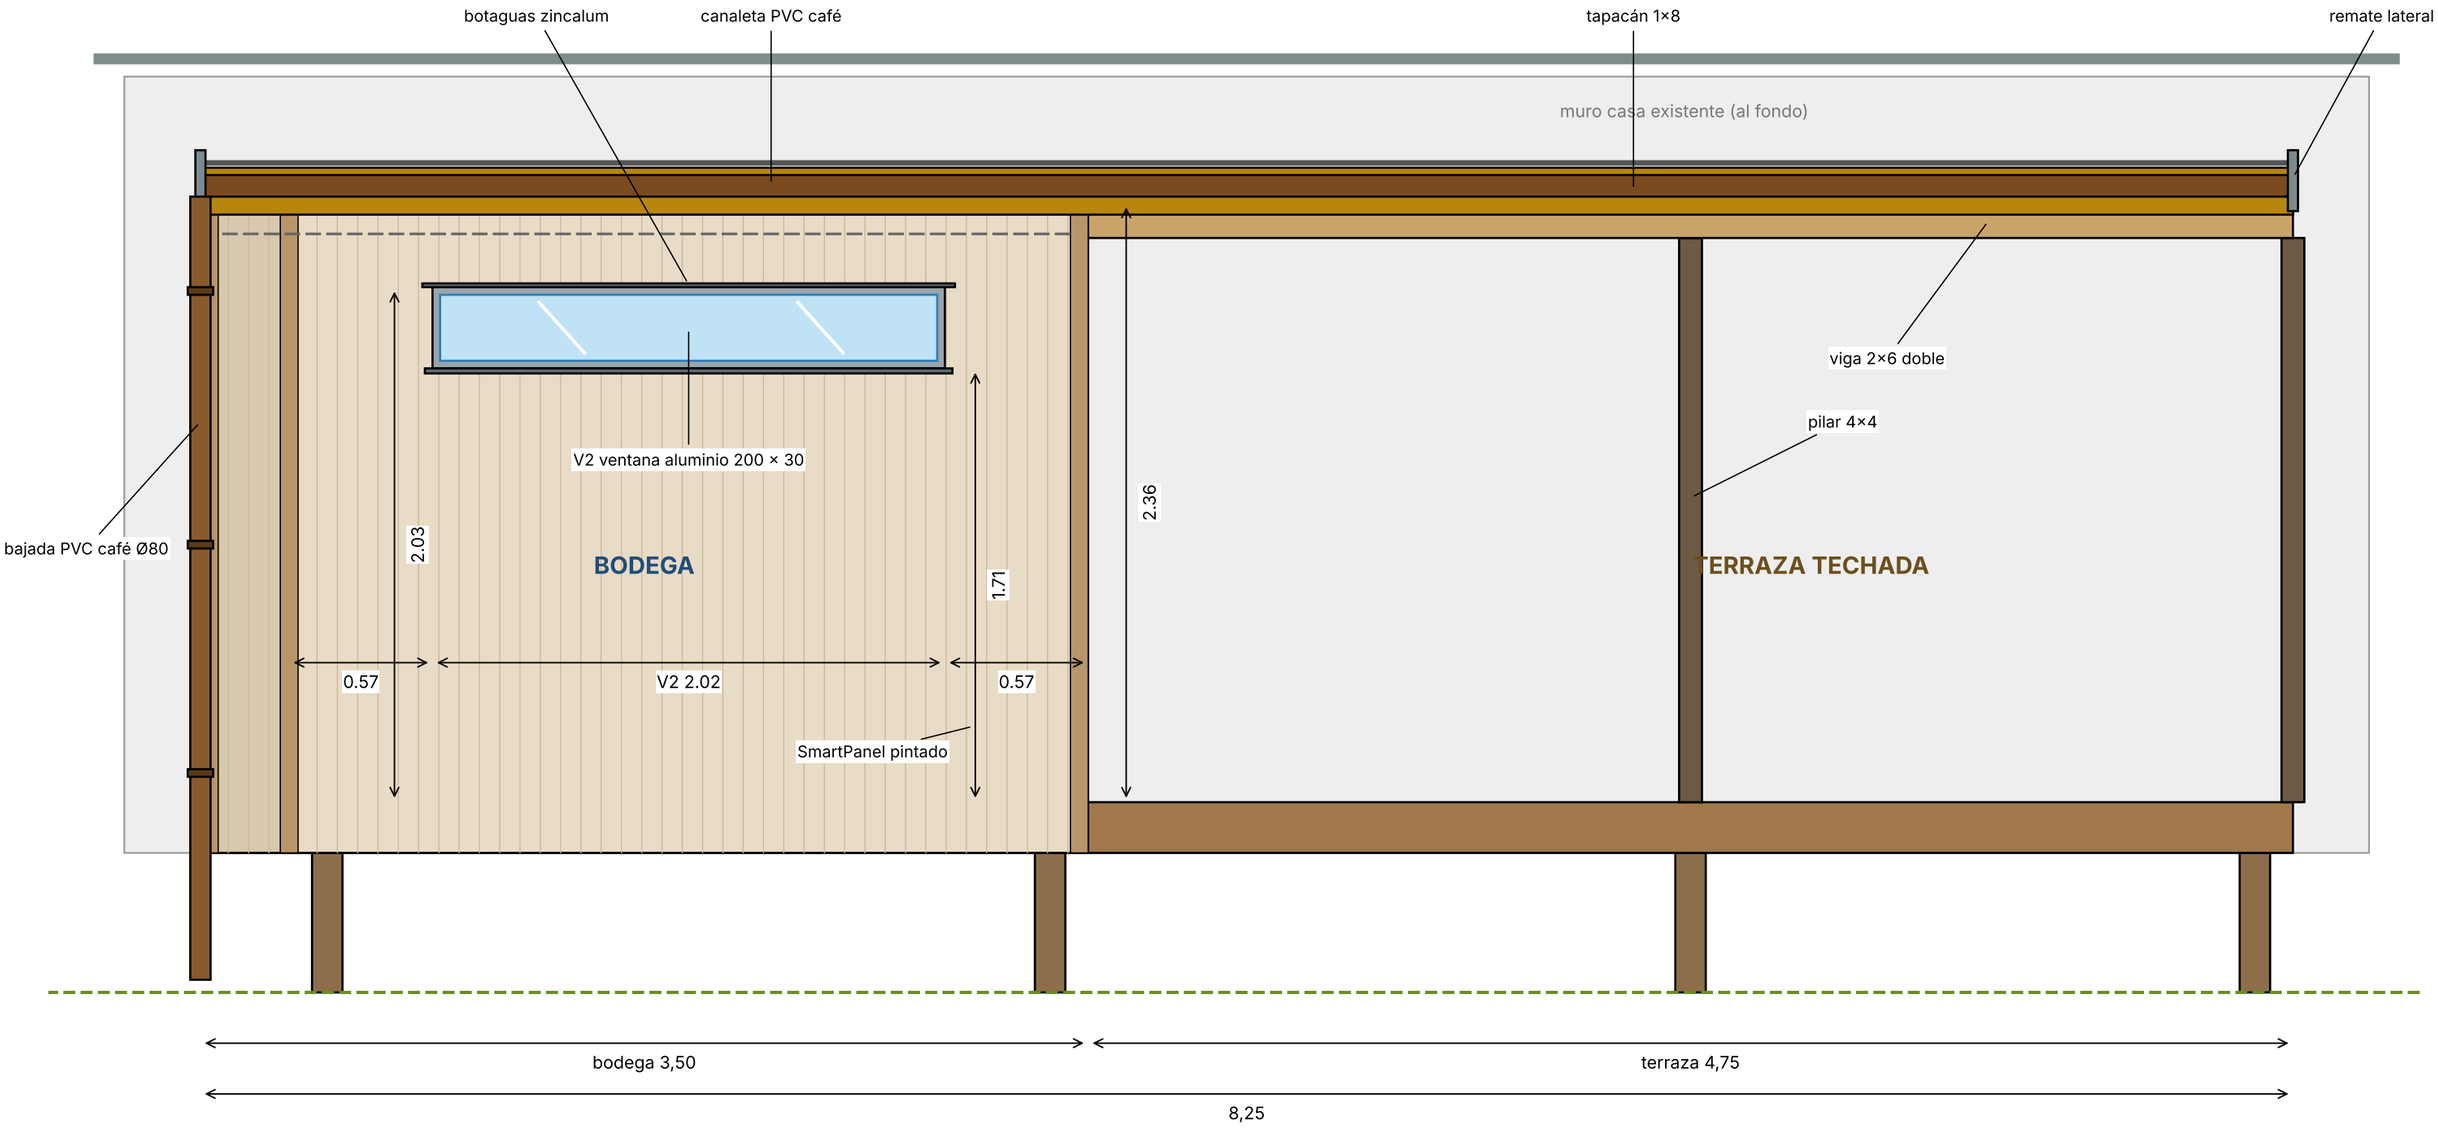


AMPLIACIÓN CABAÑA – LAGO TODOS LOS SANTOS

Lámina 9: DETALLE DE TIJERALES · Bodega 3,50 × 2,50 m + terraza techada 4,75 m · Techo rectangular, esquinas a 90° · Medidas en metros · Borrador para revisión


TIJERAL TIPO (los 15 iguales) · 2×6 pino IPV c/60 cm — elevación

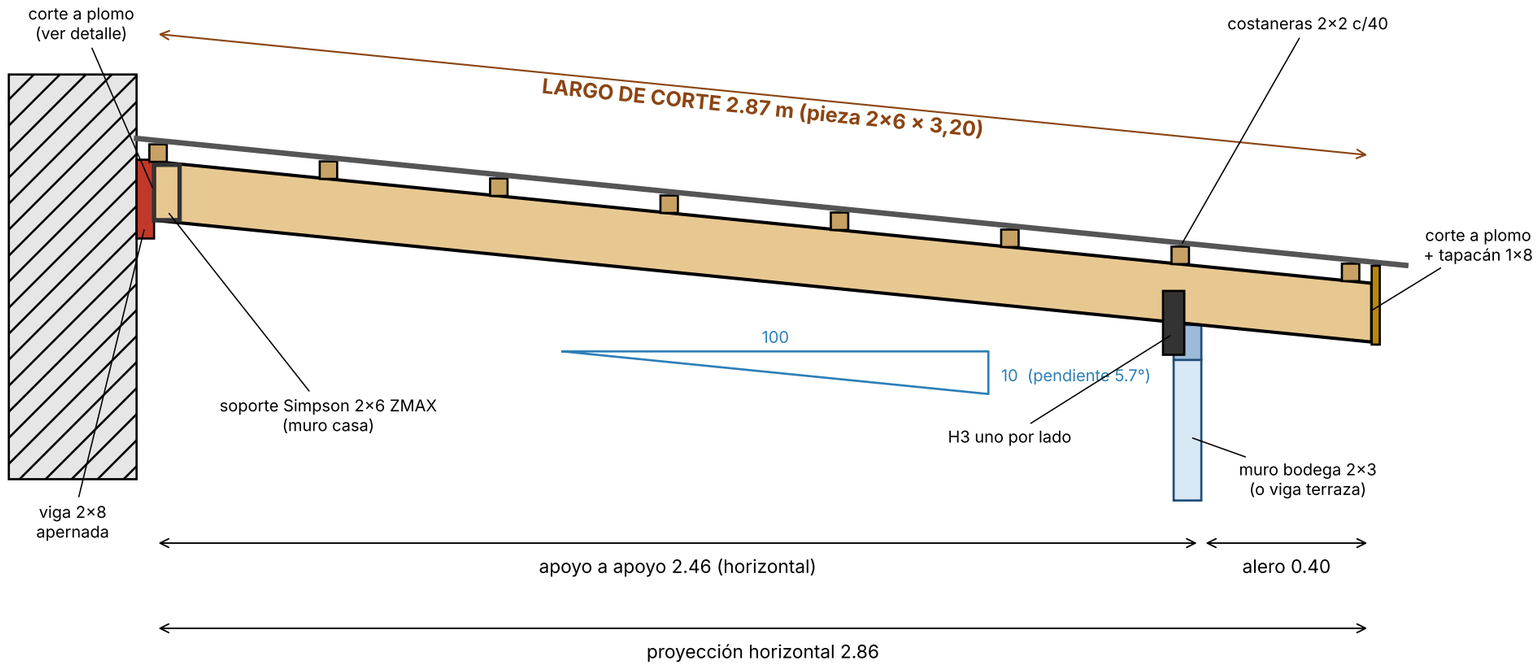

DETALLE · corte a plomo (ambos extremos)

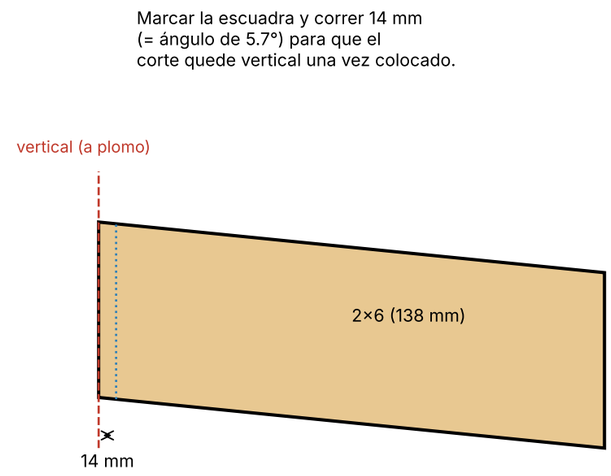

PLANTA DE TIJERALES Y APOYOS · techo rectangular, 15 tijerales iguales

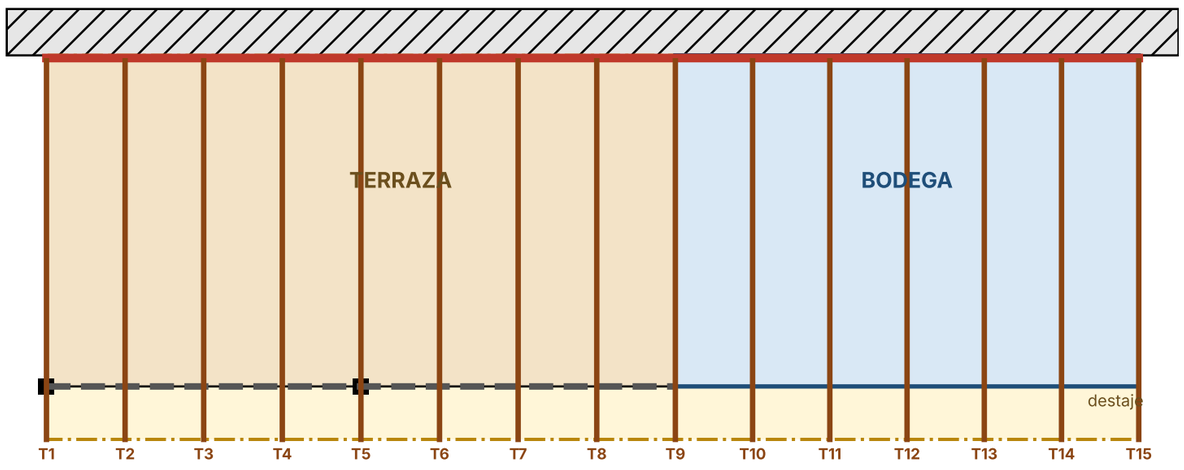

rojo: viga 2×8 + soporte Simpson · gris: viga 2×6 doble / muro bodega · ■ pilar 4×4

TABLA DE CORTE · 15 tijerales 2×6 × 3,20 (junto a la casa siempre corte a plomo, de tope en soporte Simpson)

Tijeral	Tipo	Posición	Largo corte	Apoyo ext. a	Punta	Sobrante
T1	A	0.00	2.87	2.50 (viga)	plomo	0.33
T2	A	0.59	2.87	2.50 (viga)	plomo	0.33
T3	A	1.19	2.87	2.50 (viga)	plomo	0.33
T4	A	1.78	2.87	2.50 (viga)	plomo	0.33
T5	A	2.38	2.87	2.50 (viga)	plomo	0.33
T6	A	2.97	2.87	2.50 (viga)	plomo	0.33
T7	A	3.56	2.87	2.50 (viga)	plomo	0.33
T8	A	4.16	2.87	2.50 (viga)	plomo	0.33
T9	A	4.75	2.87	2.50 (muro)	plomo	0.33
T10	A	5.33	2.87	2.50 (muro)	plomo	0.33
T11	A	5.92	2.87	2.50 (muro)	plomo	0.33
T12	A	6.50	2.87	2.50 (muro)	plomo	0.33
T13	A	7.08	2.87	2.50 (muro)	plomo	0.33
T14	A	7.67	2.87	2.50 (muro)	plomo	0.33
T15	A	8.25	2.87	2.15 (muro)	plomo (vuela 0,75)	0.33

Medidas en metros. 'Apoyo ext. a' = distancia desde el muro de la casa al muro de bodega o viga de terraza.
Los 15 tijerales son iguales (2,87 m). T15, en el destaje de la bodega, apoya a 2,15 m y vuela 0,75 m.
Junto a la casa: punta a plomo, de tope en el soporte Simpson 2×6. En el apoyo exterior: sin rebaje, 2 H3.