
AMPLIACIÓN CABAÑA – LAGO TODOS LOS SANTOS

Lámina 1: PLANTA · Bodega 3,50 × 2,50 m + terraza techada 4,75 m · Techo opción B (sigue la diagonal) · Medidas en metros · Borrador para revisión

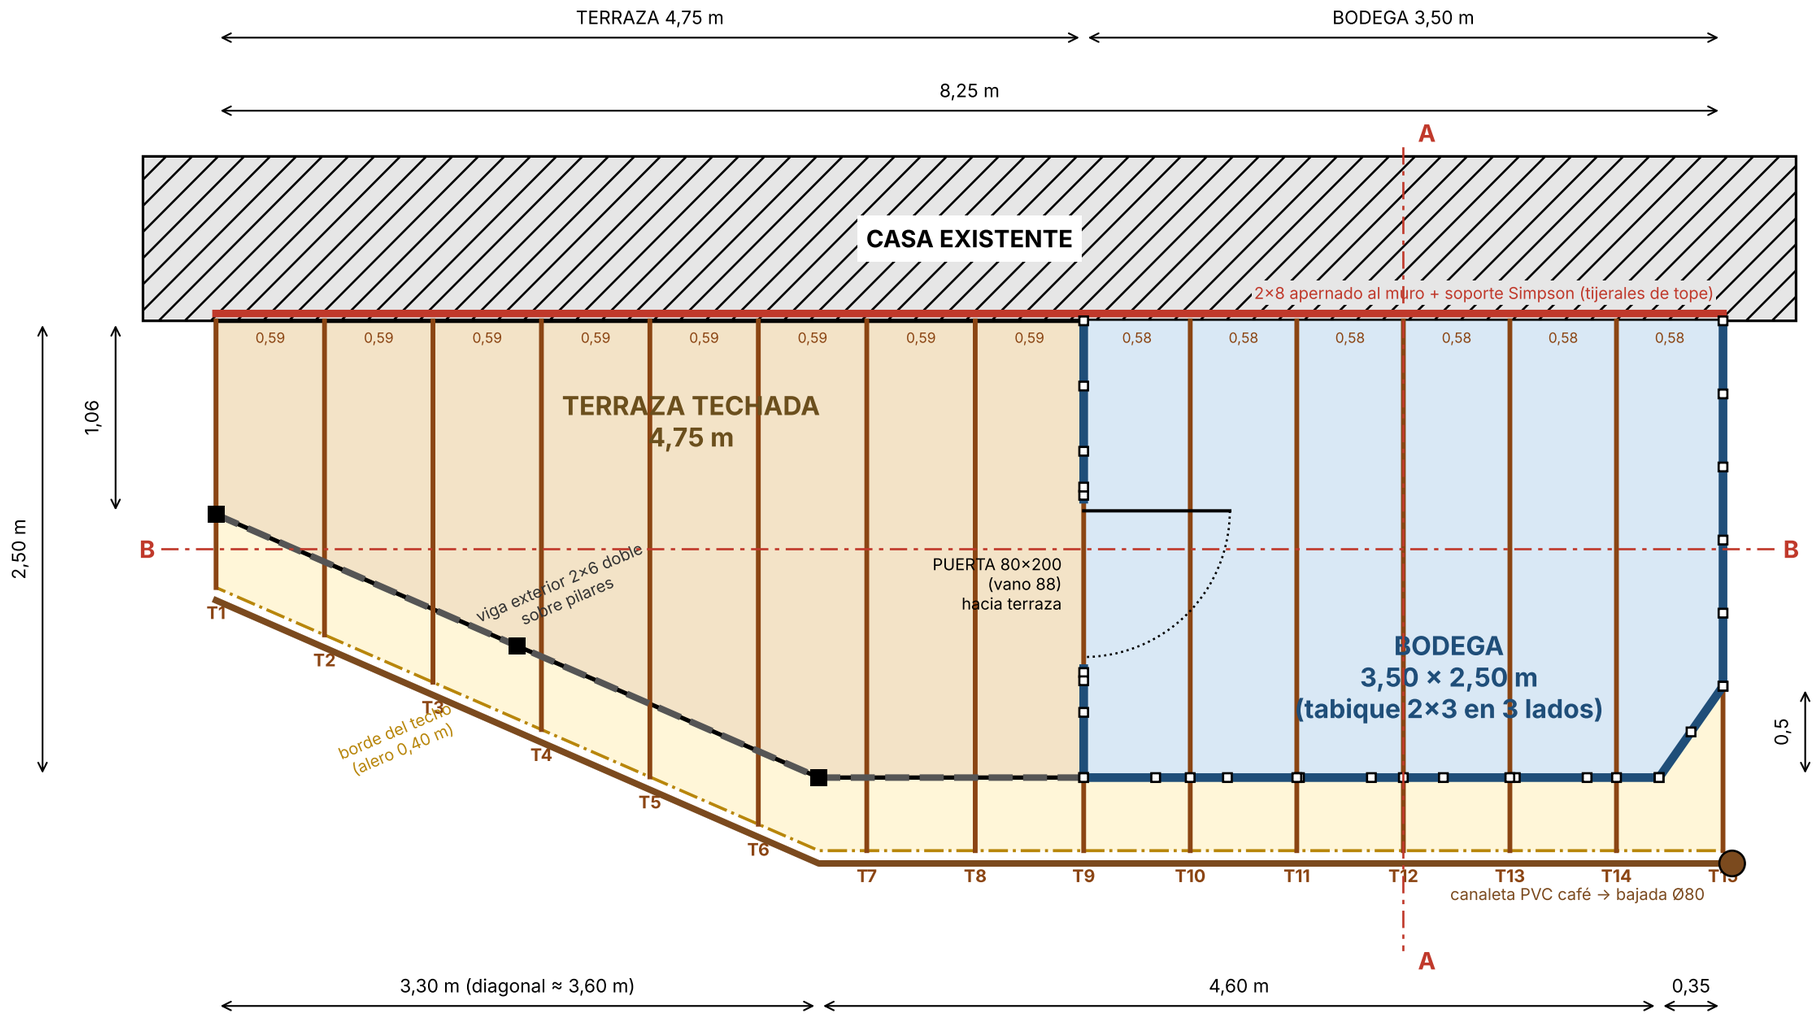

Tijeral 2×6 pino IPV

Tabique bodega 2×3 pino IPV (pies derechos c/40 cm)

Viga exterior 2×6 doble (terraza)

Borde de techo / tapacán

2×8 apernado al muro de la casa

Canaleta aguas lluvia PVC café

Pie derecho Pilar terraza 4×4

Tijerales (largo inclinado, incluye alero)


Tijeral	Posición (m)	Largo (m)	Nota
T1	0.00	1.47	corte en ángulo
T2	0.59	1.73	corte en ángulo
T3	1.19	1.99	corte en ángulo
T4	1.78	2.25	corte en ángulo
T5	2.38	2.51	corte en ángulo
T6	2.97	2.77	corte en ángulo
T7	3.56	2.91	entero
T8	4.16	2.91	entero
T9	4.75	2.91	entero
T10	5.33	2.91	entero
T11	5.92	2.91	entero
T12	6.50	2.91	entero
T13	7.08	2.91	entero
T14	7.67	2.91	entero
T15	8.25	2.91	entero

Cubierta trapezoidal (ancho útil ~1,0 m) · lista completa en lámina 4

Plancha	Desde – hasta (m)	Tipo	Largo (m)
P1	0.0 – 1.00	Translúcida	2.00
P2	1.0 – 2.00	Translúcida	2.40
P3	2.0 – 3.00	Translúcida	2.85
P4	3.0 – 4.00	Translúcida	3.00
P5	4.0 – 5.00	Translúcida	3.00
P6	5.0 – 6.00	OPACA	3.00
P7	6.0 – 7.00	Translúcida	3.00
P8	7.0 – 8.00	OPACA	3.00
P9	8.0 – 8.25	Translúcida	3.00

AMPLIACIÓN CABAÑA – LAGO TODOS LOS SANTOS

Lámina 2: ISOMÉTRICO (vista desde afuera, casa existente atrás en gris) · Bodega 3,50 × 2,50 m + terraza techada 4,75 m · Techo opción B (sigue la diagonal) · Medidas en metros · Borrador para revisión

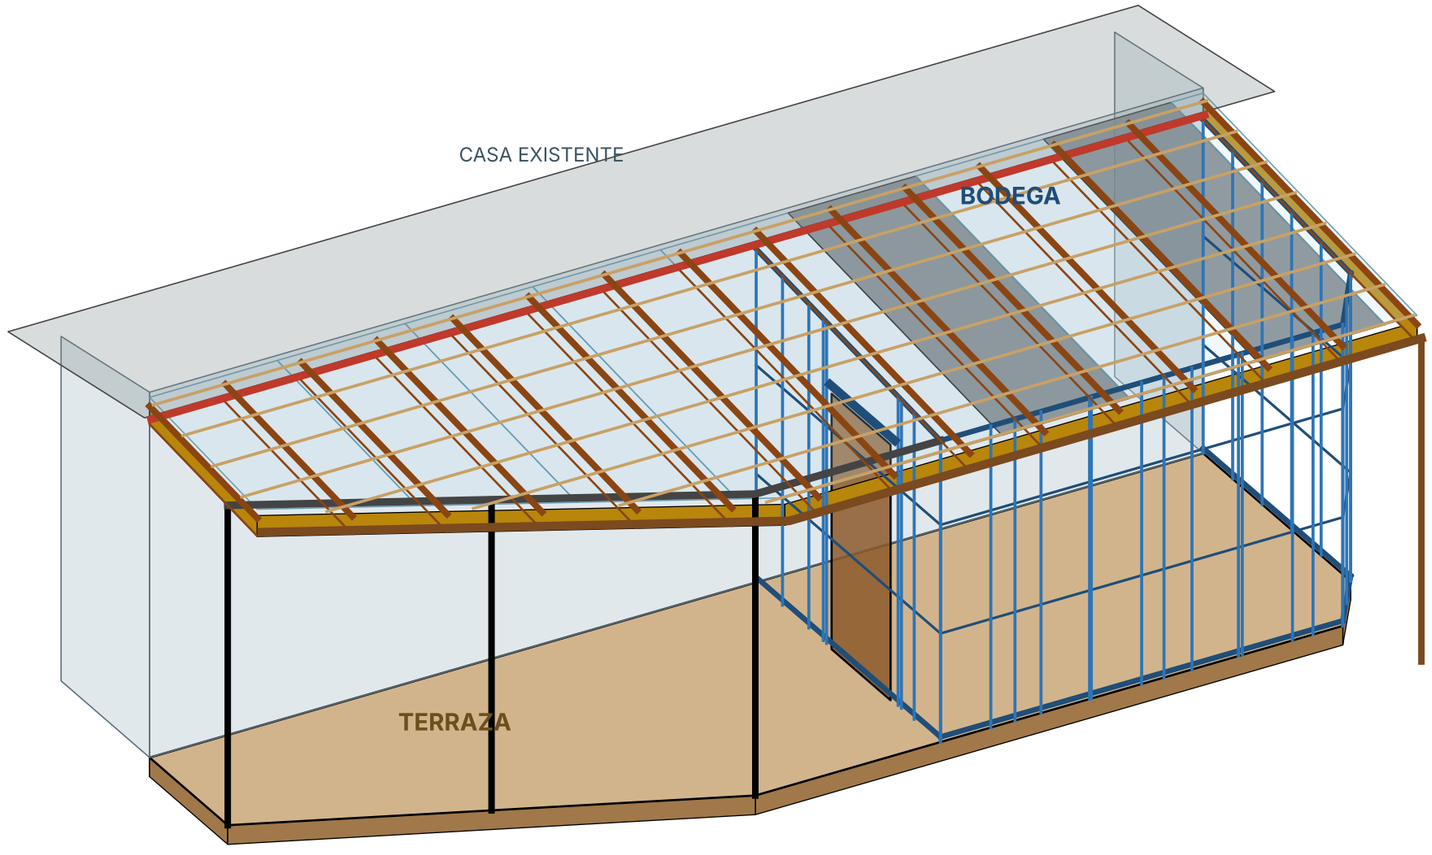


Tijerales 2×6 c/60 cm · alero 40 cm · cubierta trapezoidal translúcida en terraza e intercalada en bodega · pendiente ≈ 10 % · viga 2×8 apernada al muro (rojo) · canaleta PVC café

AMPLIACIÓN CABAÑA – LAGO TODOS LOS SANTOS

Lámina 3: CORTES · Bodega 3,50 × 2,50 m + terraza techada 4,75 m · Techo opción B (sigue la diagonal) · Medidas en metros · Borrador para revisión


CORTE TRANSVERSAL A-A (por la bodega)

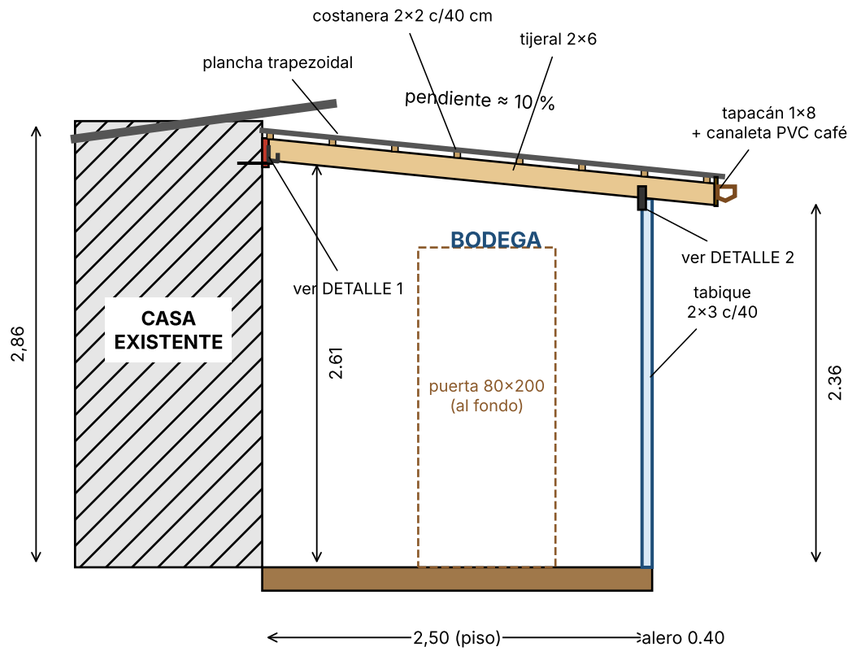


NOTAS

1. Alturas en metros desde el piso de la ampliación.
2. Junto a la casa: tijeral 2×6 DE TOPE contra viga 2×8 (41×185) apernada al muro, enrasada arriba con el tijeral, con soporte viga Simpson 2×6 ZMAX. Por fuera: sobre muro de bodega o viga 2×6 doble, con 2 soportes sismo y viento Simpson H3 por tijeral (uno por lado).
3. ALTURA MURO EXTERIOR: 2,36 m bajo el tijeral (CONFIRMADA). Así el techo pasa bajo el alero existente (2,86 m) con ≈10 % de pendiente.
4. Costaneras 2×2 cada 40 cm; plancha trapezoidal en una sola pieza (sin traslapo a lo largo).
5. Tijerales 2×6 pino IPV cada 60 cm. Cubierta translúcida en terraza e intercalada (translúcida / opaca) en bodega.
6. Bodega: tabique 2×3 IPV c/40 cm en 3 lados (contra la casa no lleva tabique), 2 corridas de cadenetas y puerta 80×200 hacia la terraza.


DETALLE 1 · apoyo en muro de la casa

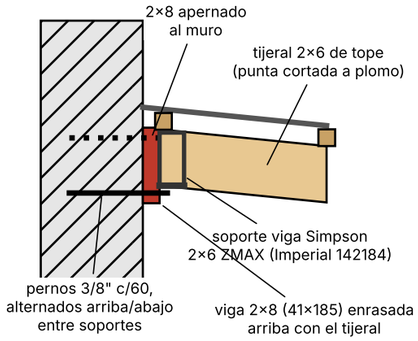

DETALLE 2 · apoyo en muro exterior

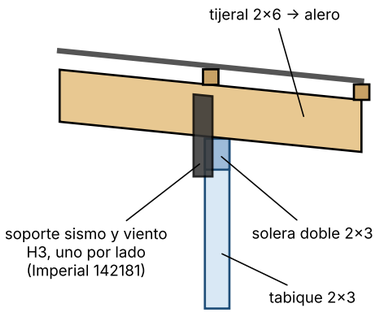

CORTE LONGITUDINAL B-B (a 1.25 m del muro, mirando hacia la casa)

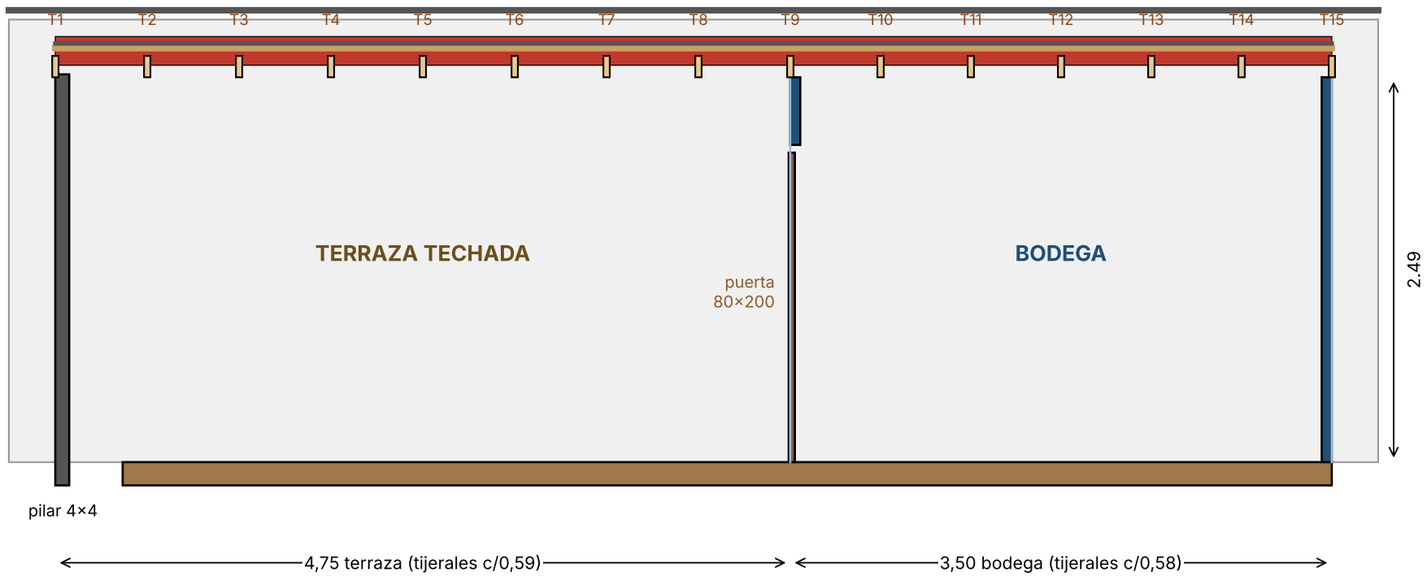

AMPLIACIÓN CABAÑA – LAGO TODOS LOS SANTOS

Lámina 4: LISTA DE MATERIALES · Bodega 3,50 × 2,50 m + terraza techada 4,75 m · Techo opción B (sigue la diagonal) · Medidas en metros · Borrador para revisión

Ítem	Material / medida	Cant.	Nota
ESTRUCTURA DE TECHO			
Tijerales c/60 cm	Pino IPV 2×6 × 3,20	15	6 se cortan en ángulo (lado diagonal)
Viga 2×8 apernada al muro (tijerales de tope)	Pino IPV 2×8 × 3,20	3	de canto, enrasada con tijeral
Pernos o tirafondos 3/8"	c/60 cm	15	según material del muro existente
Soporte viga madera cepillada 2×6 ZMAX	Simpson · Imperial SKU 142184	15	1 por tijeral, en muro casa
Soporte sismo y viento H3	Simpson · Imperial SKU 142181	30	2 por tijeral (uno por lado)
Costaneras c/40 cm	Pino IPV 2×2 × 3,20	21	8 corridas
Tapacán vertical	Tabla pino 1×8 × 3,20	4	diagonal 3,60 + recto 4,95; pintar
Bloqueos entre tijerales (muro bodega)	Pino IPV 2×6 × 3,20	1	
TERRAZA			
Viga exterior doble (sigue la diagonal)	Pino IPV 2×6 × 3,20	4	unir sobre pilar
Pilares	Pino IPV 4×4 × 3,20	3	
CUBIERTA TRAPEZOIDAL			
Plancha translúcida (policarbonato)	largos: 2.00, 2.40, 2.85, 3.00, 3.00, 3.0	7	mismo perfil que la opaca
Plancha opaca (zinc-alum)	largos: 3.00, 3.00	2	intercalada en bodega
HOJALATERÍA DE REMATE (zincalum 0,4 mm)			
Plancha lisa para plegar	zincalum 1,00 × 3,00 m	3	el hojalatero pliega forros y remates
Forro contra muro existente	desarrollo ~40 cm x 3 m	3	8,25 m + traslapos (DETALLE 3)
Remate lateral	desarrollo ~35 cm	2	2,9 m y 1,5 m (DETALLE 4)
Cierre de espuma perfil trapezoidal	tira ~1 m	9	bajo el forro, junto al muro
Sellante poliuretano	cartucho	2	borde superior del forro
AGUAS LLUVIA (PVC café)			
Canaleta PVC café 110 mm	x 4,00 m	3	8,55 m de borde (diagonal + recto)
Uniones de canaleta	PVC café	3	incluye quiebre de la diagonal
Tapas de canaleta	PVC café	2	
Salida a bajada	PVC café Ø80	1	extremo derecho (esquina bodega)
Ganchos de canaleta	PVC café	19	c/50 cm, al tapacán 1×8
Tubo de bajada	PVC café Ø80 × 3 m	2	confirmar altura al terreno
Codos de bajada	PVC café Ø80	3	2 para el alero + 1 al final
Abrazaderas de bajada	PVC café Ø80	3	
Sellante para PVC / silicona	cartucho	1	


Ítem	Material / medida	Cant.	Nota
BODEGA – ESTRUCTURA			
Pies derechos c/40 cm	Pino IPV 2×3 × 3,20	36	incluye vano y esquinas
Soleras (inferior + superior doble)	Pino IPV 2×3 × 3,20	9	
Cadenetas (2 corridas)	Pino IPV 2×3 × 3,20	6	
Dintel puerta (de canto)	Pino IPV 2×4 × 3,20	1	
Puerta exterior + marco	80 × 200 cm	1	bisagras 3 × 3½" + cerradura
Escuadras metálicas base pilares	galvanizadas	6	2 por pilar
TORNILLOS (sin clavos · detalle en planilla Excel)			
Tornillo madera 8 × 3" zincado		890	
Tirafondo 1/4" x 4" zincado		50	
Tornillo Simpson SD #9 × 1½" (para conectores)		440	
Tirafondo 3/8" x 4½" + golilla		20	
Autoperforante techo punta aguja 12 × 1½" c/golilla		340	
Autoperforante costura 1/4" x 7/8"		70	
Tornillo exterior 8 × 2" galvanizado		690	
Tornillo madera 6 × 1¼"		330	
Tornillo 6 × 1" (cortagotera)		20	
BODEGA – REVESTIMIENTOS			
SmartPanel exterior	1,22 × 2,44	11	~18 m², pintar
Contrachapado ranurado interior	1,22 × 2,44	10	~18 m² (sin muro de la casa)
Barrera de humedad (Tyvek/fieltro)	rollo	1	detrás del SmartPanel
Esquineros / tapajuntas	2,40 m	5	
Cortagotera en Z	3,00 m	3	unión de franja superior
Grapas para barrera de humedad	caja	1	corchetera

Cantidades de madera con ~10 % de pérdida (tijerales justos). Confirmar ancho útil y largos disponibles de las planchas en la tienda.


AMPLIACIÓN CABAÑA – LAGO TODOS LOS SANTOS

Lámina 5: HOJALATERÍA DE REMATE · Bodega 3,50 × 2,50 m + terraza techada 4,75 m · Techo opción B (sigue la diagonal) · Medidas en metros · Borrador para revisión


UBICACIÓN DE LA HOJALATERÍA (planta de techo)

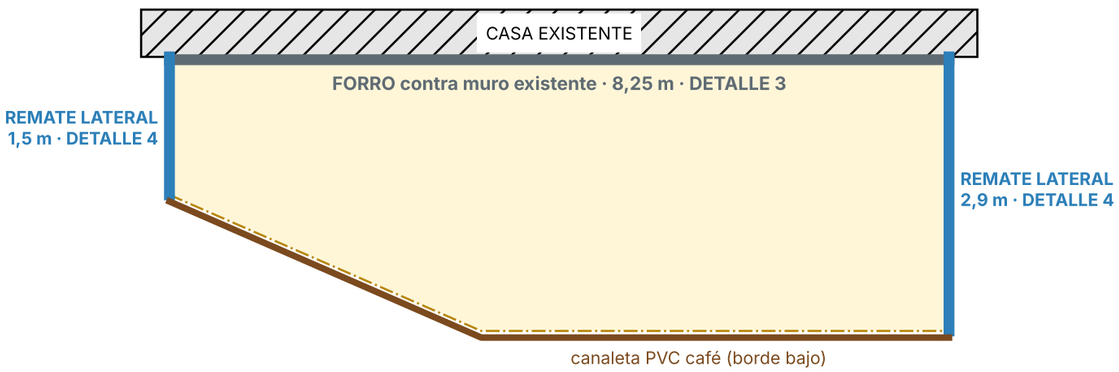

DETALLE 3 · forro contra el muro existente

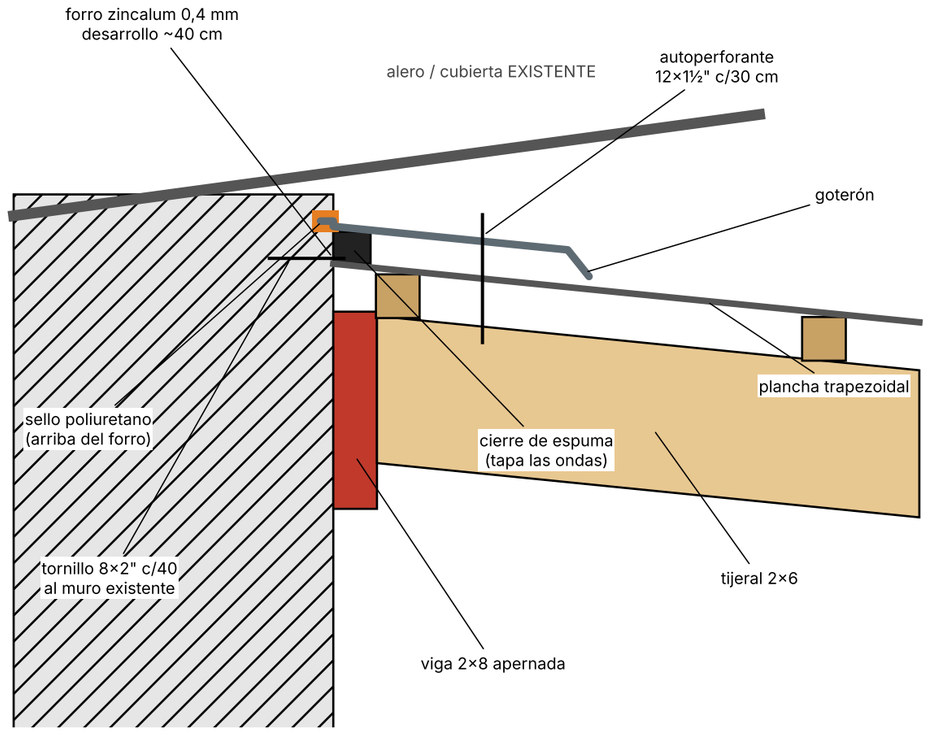

DETALLE 4 · remate lateral (bordes de 2,5 m y 1,06 m)

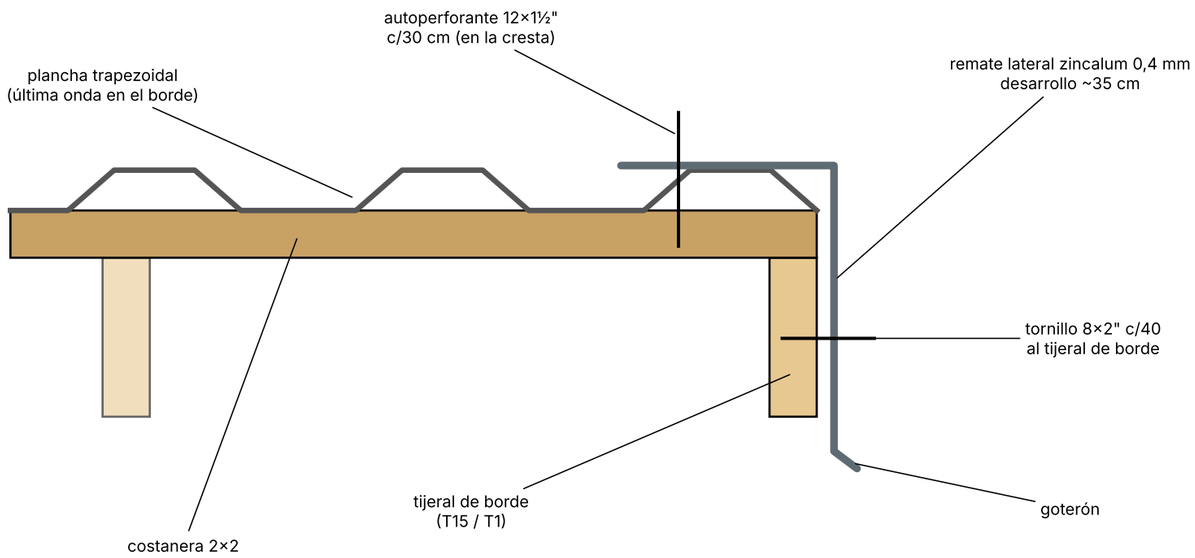

NOTAS HOJALATERÍA

1. Hojalatería en zincalum liso 0,4 mm, plegada por hojalatero.
2. FORRO (DETALLE 3): va contra el muro existente, bajo el alero de la casa, en los 8,25 m. Baja por el muro y monta ~20 cm sobre la plancha. Arriba lleva sello de poliuretano; abajo, goterón.
3. Bajo el forro, una tira de cierre de espuma tapa las ondas de la plancha trapezoidal para que no entre agua ni viento.
4. REMATE LATERAL (DETALLE 4): en los dos bordes perpendiculares a la casa (2,9 m lado bodega y 1,5 m lado terraza). Cubre la última onda y baja por la cara del tijeral de borde, con goterón.
5. Traslapos entre piezas de hojalatería: mínimo 10 cm, con sello.
6. Fijación: autoperforante 12×1½" con golilla en la cresta (c/30 cm) y tornillo exterior 8×2" al muro / tijeral (c/40 cm). Sin clavos.